


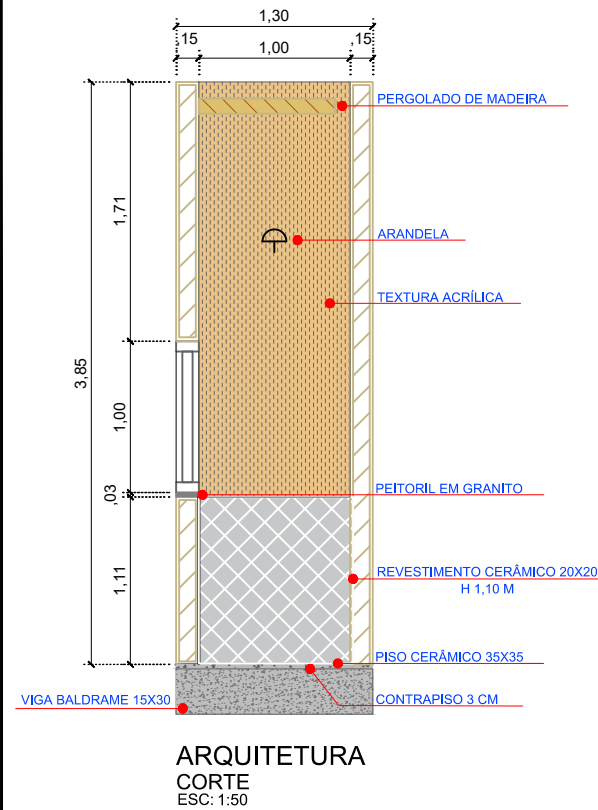
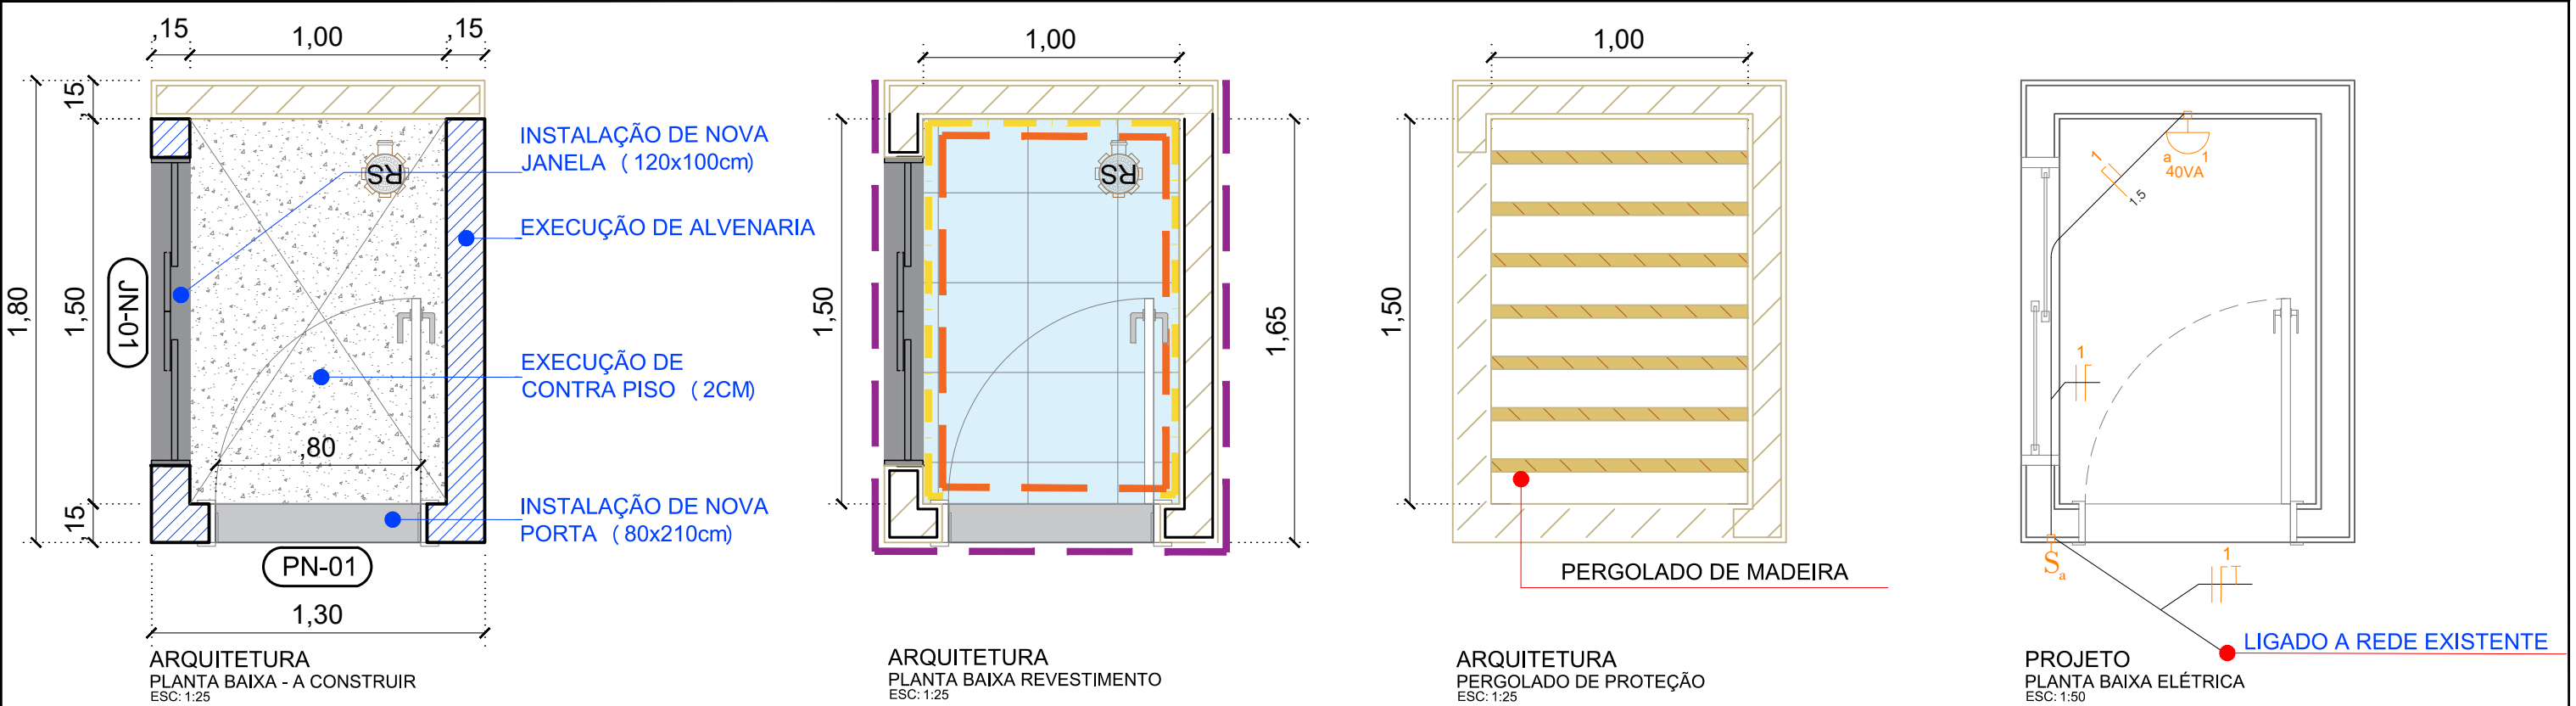


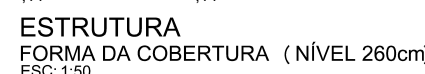

LEGENDA		PORTA NOVA						
	PONTO DE LUZ INCANDESCENTE NA PAREDE	TIPO :	LARGURA (cm):	ALTURA (cm):	QTD :	MATERIAL :	OBSERVAÇÃO :	AMBIENTE :
	INTERRUPTOR SIMPLES	PN-01	87	210	01	ALUMÍNIO / VIDRO	DE ABRIR - GIRO COM POSTIGO	POÇO DE VENTILAÇÃO
	DUTO PASSANDO SOB O FORRO OU PELA PAREDE - Ø=3/4"	JANELA NOVA						
	INDICACAO DE FIOS NA TUBULACAO (NA ORDEM, FASE, NEUTRO, RETORNO E TERRA.)	TIPO :	DIMENSÕES (L x H)	PEITORIL	QTD :	MATERIAL :	OBSERVAÇÃO :	AMBIENTE :
	MARCAÇÃO DOS CIRCUITOS	JN-01	120x100	110	01	ALUMÍNIO / VIDRO	DE CORRER	POÇO DE VENTILAÇÃO
PAREDE		NOTA:						
	IMPERMEABILIZAÇÃO H = 1,10 M + CHAPISCO + EMBOÇO + REVESTIMENTO CERÂMICO PARA PAREDES 20X20 CM ATÉ 1,10 M	O POÇO DE VENTILAÇÃO DEVERÁ GARANTIR VENTILAÇÃO NATURAL PERMANENTE, ILUMINAÇÃO E RENOVAÇÃO DE AR DOS AMBIENTES ATENDIDOS, CONFORME DIMENSÕES E POSICIONAMENTO DEFINIDOS EM PROJETO ARQUITETÔNICO						
	CHAPISCO + MASSA ÚNICA + FUNDO SELADOR + PINTURA COM TINTA TEXTURIZADA ACRÍLICA, UMA COR ACIMA DO REVESTIMENTO	AS PAREDES INTERNAS DO POÇO DEVERÃO RECEBER ACABAMENTO IMPERMEÁVEL E DE FÁCIL MANUTENÇÃO, ASSEGURANDO DURABILIDADE E RESISTÊNCIA À UMIDADE						
	CHAPISCO + MASSA ÚNICA + FUNDO SELADOR + PINTURA COM TINTA ACRÍLICA, UMA COR	O POÇO DEVERÁ POSSUIR 01 (UMA) JANELA, DESTINADA À VENTILAÇÃO E ILUMINAÇÃO NATURAL, INSTALADA CONFORME NORMAS DE ESQUADRIAS, ASSEGURANDO ESTANQUEIDADE E CORRETO FUNCIONAMENTO						
	PAREDE A CONSTRUIR	DEVERÁ SER INSTALADO RALO NO PISO DO POÇO, CONECTADO À REDE DE DRENAGEM PLUVIAL OU SISTEMA DE ESCOAMENTO PREVISTO EM PROJETO, GARANTINDO O ADEQUADO ESCOAMENTO DE ÁGUAS PLUVIAIS E DE LAVAGEM						
	CONTRAPISO EM ARGAMASSA TRAÇO 1:4 ESPESSURA: 2CM	O PISO DO POÇO DEVERÁ POSSUIR DECLIVIDADE MÍNIMA DIRECIONADA AO RALO, EVITANDO ACÚMULO DE ÁGUA						
	REVESTIMENTO CERÂMICO 35X35 PARA PISO (ÁREAS MOLHADAS) PADRÃO POPULAR	DEVERÁ SER INSTALADA GRADE DE PROTEÇÃO EM MADEIRA, FIXADA DE FORMA SEGURA, ASSEGURANDO PROTEÇÃO CONTRA ACESSO INDEVIDO, SEM COMPROMETER A VENTILAÇÃO						
		TODOS OS ELEMENTOS EM MADEIRA DEVERÃO RECEBER TRATAMENTO PRESERVATIVO CONTRA UMIDADE, FUNGOS E INSETOS, CONFORME NORMAS APLICÁVEIS						
		AS INTERFACES ENTRE ESQUADRIAS, ALVENARIA E ELEMENTOS DE DRENAGEM DEVERÃO RECEBER VEDAÇÃO ADEQUADA, PREVENINDO INFILTRAÇÕES E PATOLOGIAS						
		GRUPO: CONSTRUÇÃO, AMPLIAÇÃO E ADEQUAÇÃO DE CÔMODOS						FOLHA:
		KIT: POÇO DE VENTILAÇÃO						01/03
		CÓDIGO DO KIT: 4.5						


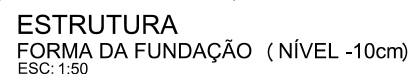


		POS	BIT (mm)	QUANT	COMPRIMENTO		Pilares (2x) de 385 e (2x) de 385						
					UNIT (cm)	TOTAL (cm)		50A	5	10	4	385	3080
Estacas (4x)								50A	6	10	4	385	3080
								50A	7	6.3	120	72	8640
	50A	1	10	5	180	3600	Viga baldrame						
	50A	2	6.3	12	72	3456							
Bloco de fundação (4x)								50A	8	8	4	179	716
								50A	9	8	4	203	812
	50A	3	8	4	150	2400		50A	10	8	4	203	812
	50A	4	8	4	160	2560		50A	12	6.3	19	80	1520
MINISTÉRIO DAS CIDADES 		GRUPO: CONSTRUÇÃO, AMPLIAÇÃO E ADEQUAÇÃO DE CÔMODOS											FOLHA 02/03
		KIC: POCO DE VENTILAÇÃO							CÓDIGO DO KIT: 4.5				

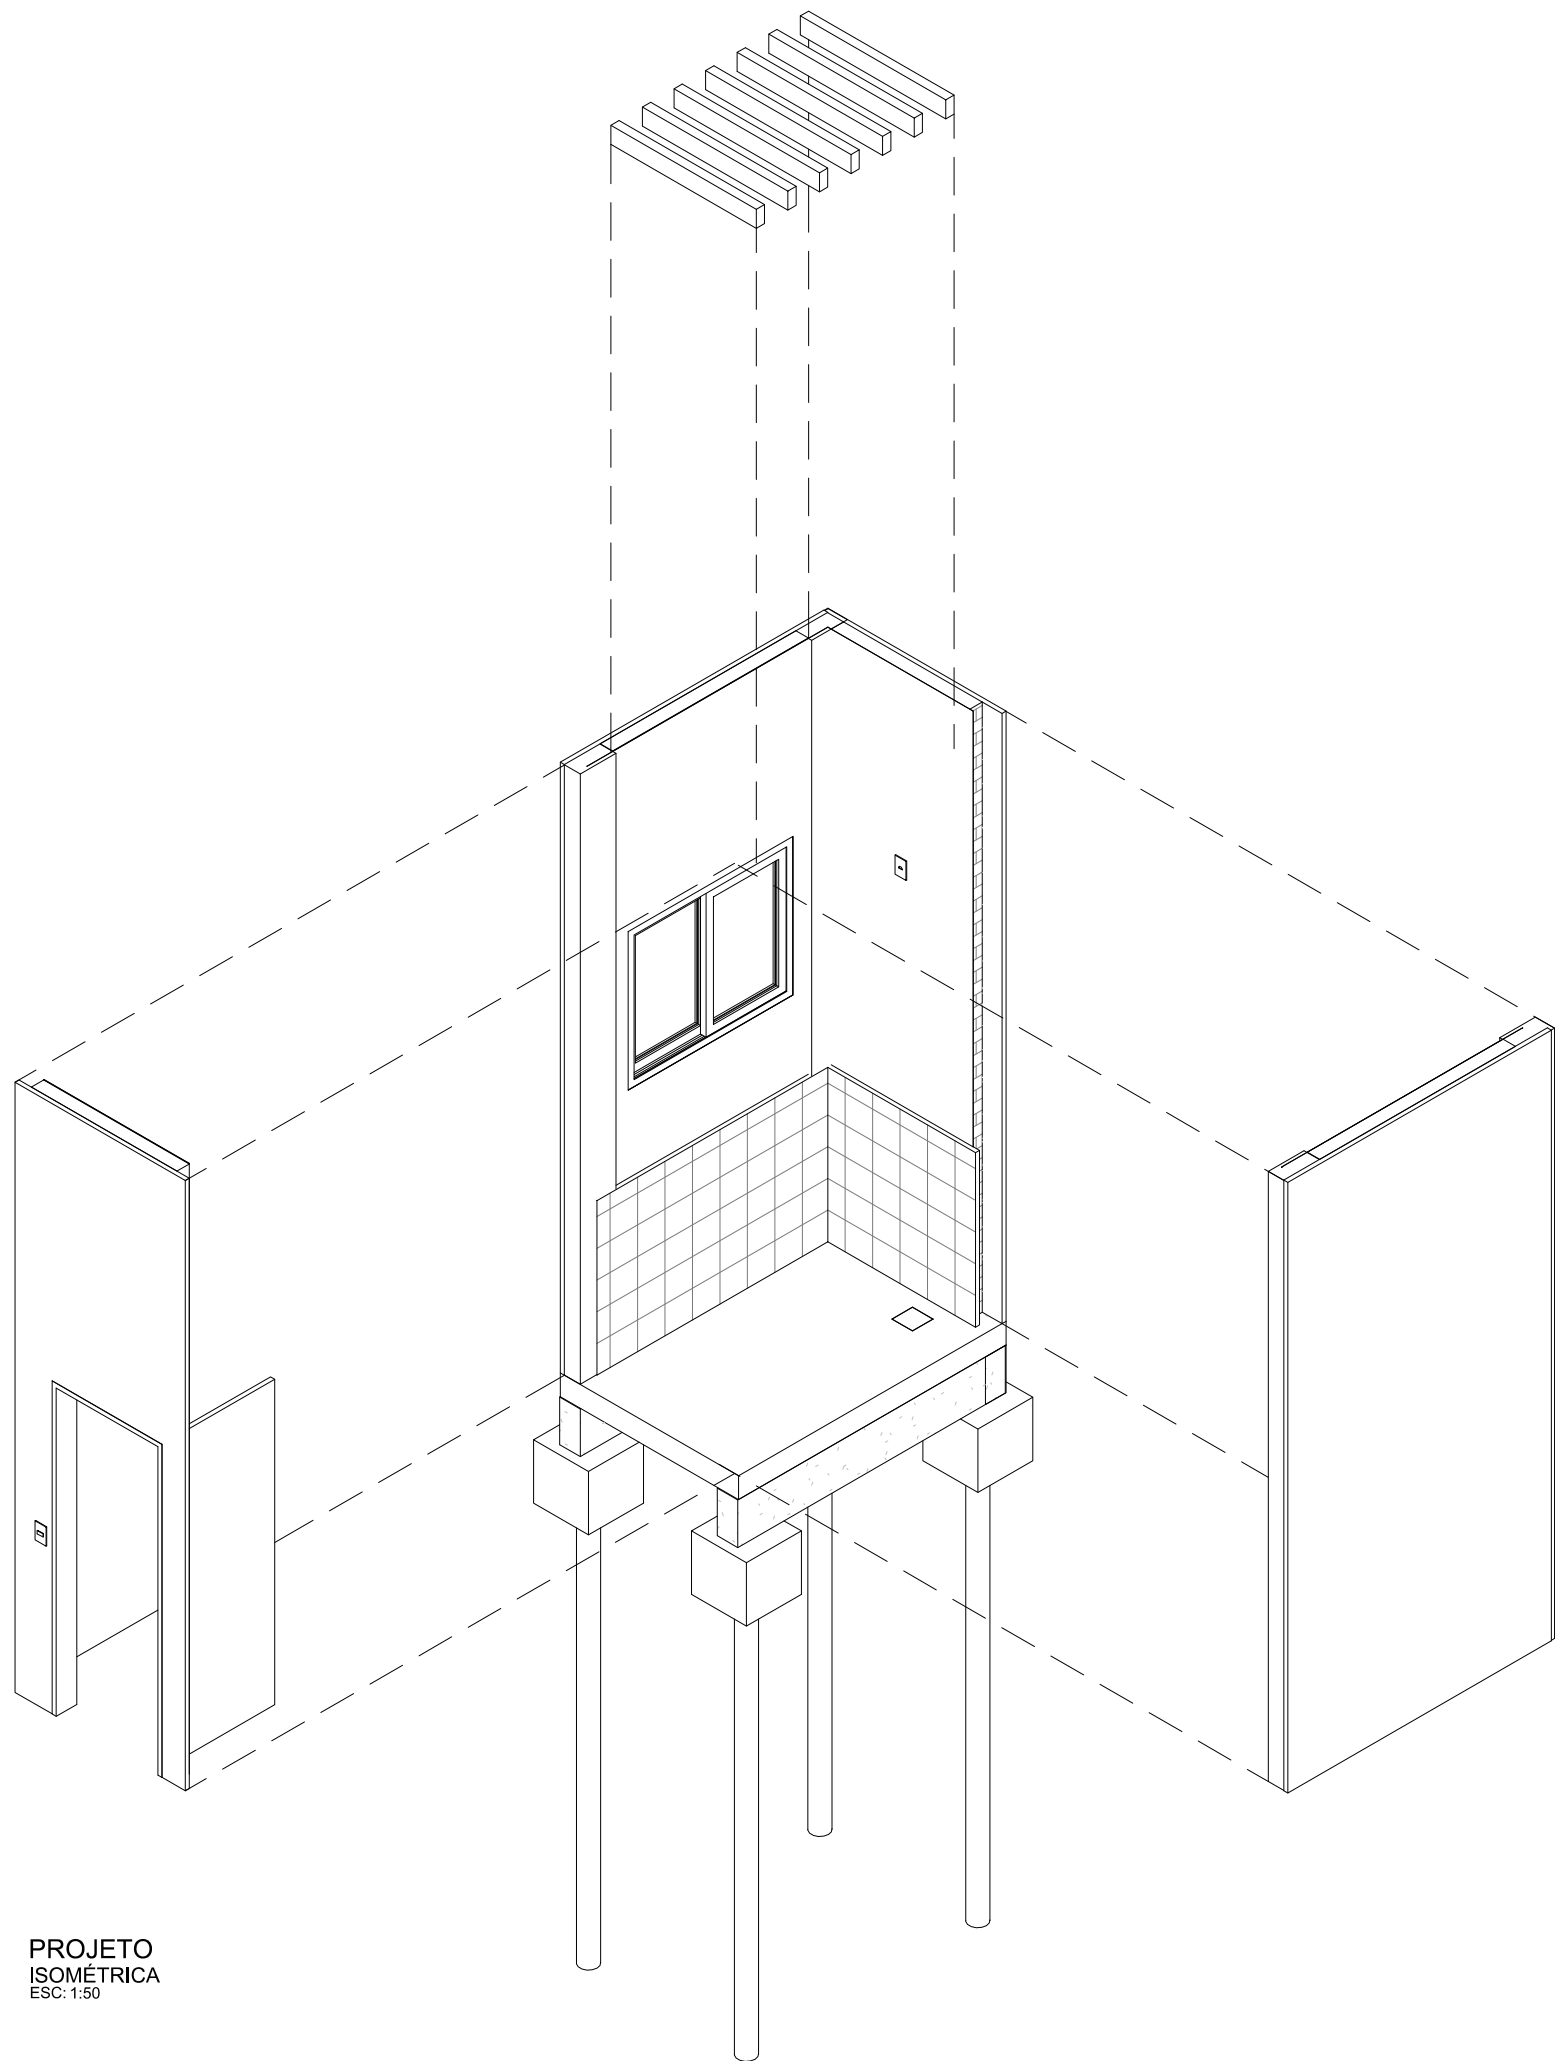

PROJETO
ISOMÉTRICA
ESC: 1:50

B1=B2=B3=B4

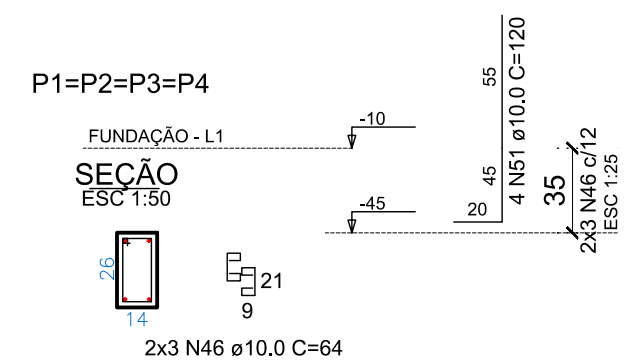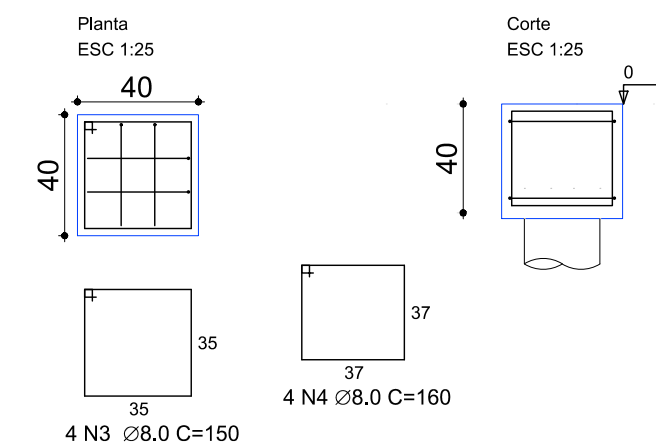

ESTRUTURA
DETALHES DOS BLOCOS 40x40x40
ESC: 1:25