




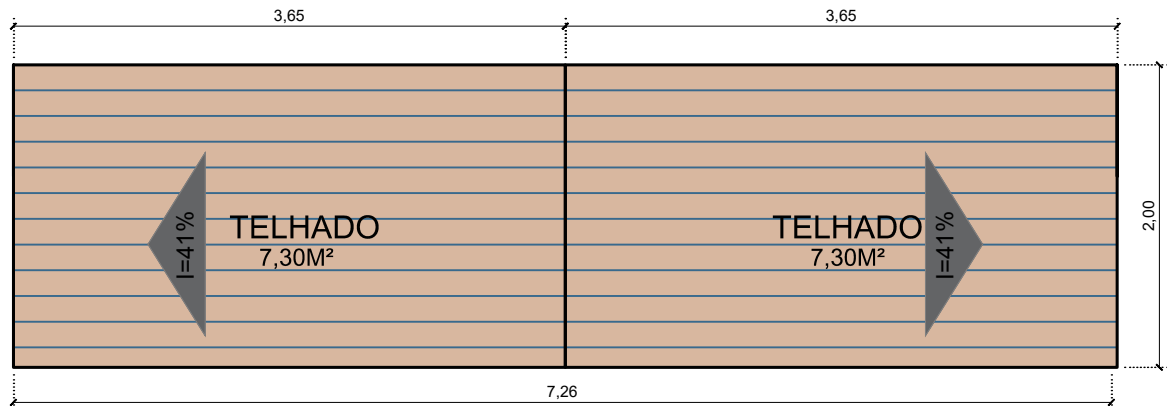

COBERTURA
COBERTURA EM TELHA CERÂMICA
ESC: 1:50

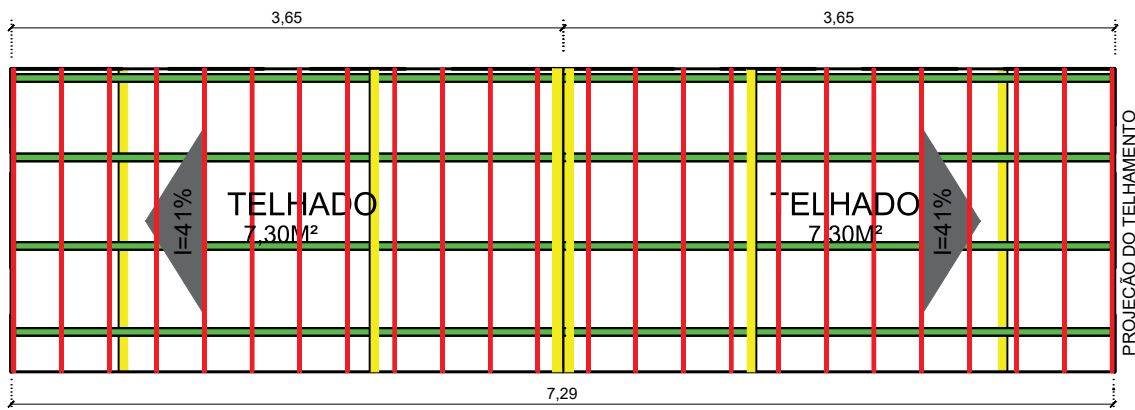

COBERTURA
ESTRUTURA DA COBERTURA
ESC: 1:50

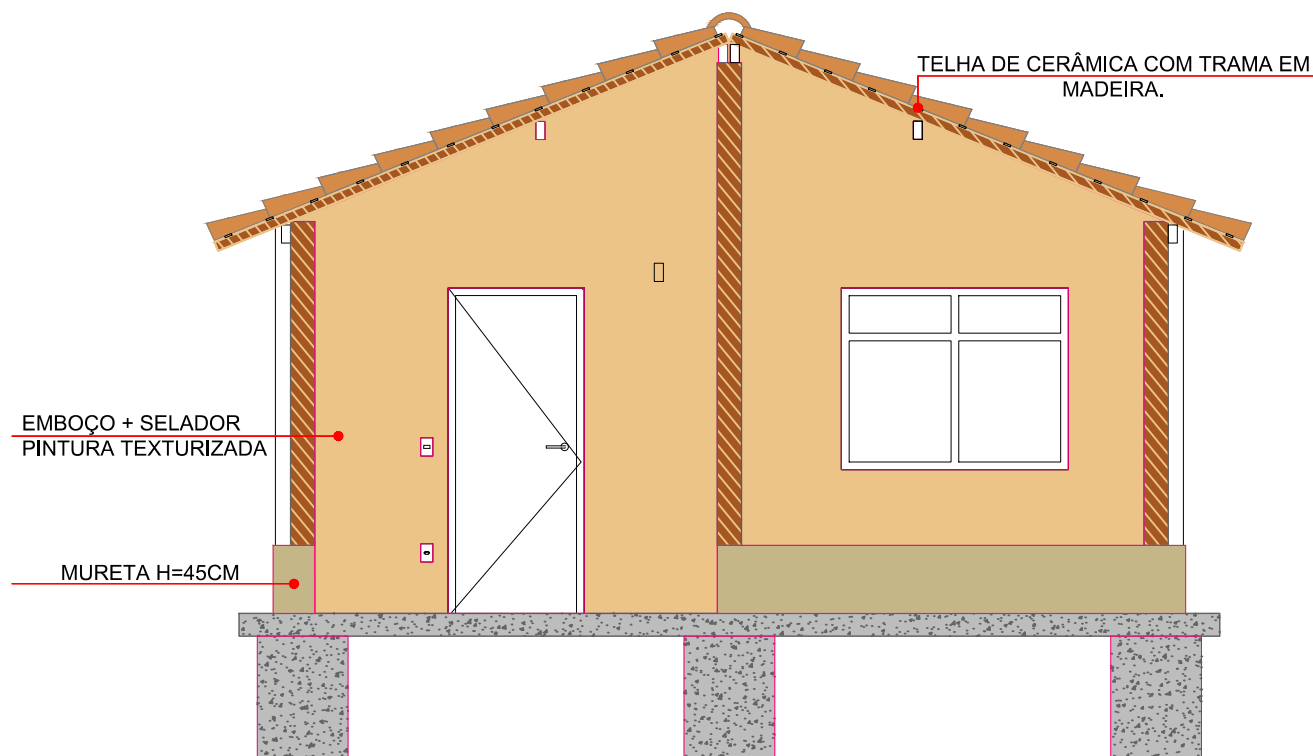

PROJETO
CORTE
ESC: 1:50

LEGENDA		QUADRO DE QUANTITATIVO			
	MADEIRA	MADEIRA	QUANTIDADE DE PEÇAS	M LINEAR POR PEÇA	SOMA TOTAL
	RIPA 1,5 x 5,0 cm;	RIPA 1,5 x 5,0 cm;	24	4,31 m	103,44 m
	CAIBRO 5,0 x 6,0 cm;	CAIBRO 5,0 x 6,0 cm;	16	3,64 m	58,24 m
	TERÇA 6,0 x 12,0 cm;	TERÇA 6,0 x 12,0 cm;	6	4,31 m	25,86 m

NOTA:

AS TRAMAS DA ESTRUTURA DA COBERTURA DEVERÃO SER EXECUTADAS RIGOROSAMENTE CONFORME INDICADO EM PROJETO E NO RESPECTIVO QUADRO DE LEGENDAS, OBSERVANDO-SE AS SEGUINTE ESPECIFICAÇÕES:

- RIPAS EM MADEIRA DE LEI, COM SEÇÃO NOMINAL DE 1,5 x 5,0 CM, ESPAÇADAS A 0,40 M ENTRE EIXOS;
- CAIBROS EM MADEIRA DE LEI, COM SEÇÃO NOMINAL DE 5,0 x 6,0 CM, ESPAÇADOS A 0,45 M ENTRE EIXOS;
- TERÇAS EM MADEIRA DE LEI, COM SEÇÃO NOMINAL DE 6,0 x 12,0 CM, COM ESPAÇAMENTO ENTRE EIXOS VARIANDO DE 1,50 M A 2,00 M, CONFORME DETALHAMENTO EM PROJETO.

AS MADEIRAS UTILIZADAS DEVERÃO SER DO TIPO MASSARANDUBA, ANGELIM OU ESPÉCIE EQUIVALENTE DISPONÍVEL NA REGIÃO, FORNECIDAS EM ESTADO BRUTO, ISENTAS DE DEFEITOS QUE COMPROMETAM SUA RESISTÊNCIA E DESEMPENHO ESTRUTURAL


A COBERTURA DEVERÁ SER EXECUTADA COM DECLIVIDADE ENTRE 32% E 40%, CONFORME INDICADO EM PROJETO. CASO SEJA NECESSÁRIA A ADOÇÃO DE DECLIVIDADE SUPERIOR, ESTA SOMENTE SERÁ ADMITIDA DESDE QUE AS TELHAS SEJAM CORRETAMENTE FIXADAS À ESTRUTURA DE APOIO, POR MEIO DE AMARRAÇÃO COM ARAME GALVANIZADO, UTILIZANDO A ORELHA PRÓPRIA DAS TELHAS.

A FIXAÇÃO DEVERÁ ATENDER ÀS RECOMENDAÇÕES TÉCNICAS E AOS CRITÉRIOS ESTABELECIDOS NA ABNT NBR 8039, GARANTINDO A ADEQUADA ESTABILIDADE, SEGURANÇA E DESEMPENHO DO SISTEMA DE COBERTURA.


PARA A QUANTIFICAÇÃO DOS SERVIÇOS DE CHAPISCO, MASSA ÚNICA, APLICAÇÃO DE SELADOR, MASSA CORRIDA E PINTURA, ADOTA-SE A ALTURA DE REFERÊNCIA DE 2,70 M, MEDIDA A PARTIR DO PISO ACABADO;

NO CÁLCULO DAS ÁREAS DE PINTURA, DEVERÃO SER CONSIDERADOS OS DESCONTOS DOS VÃOS DE PORTAS E JANELAS, EM CONFORMIDADE COM OS CRITÉRIOS TÉCNICOS DE MEDIÇÃO;


TODAS AS DIMENSÕES DEVERÃO SER CONFERIDAS IN LOCO ANTES DA EXECUÇÃO DOS SERVIÇOS.

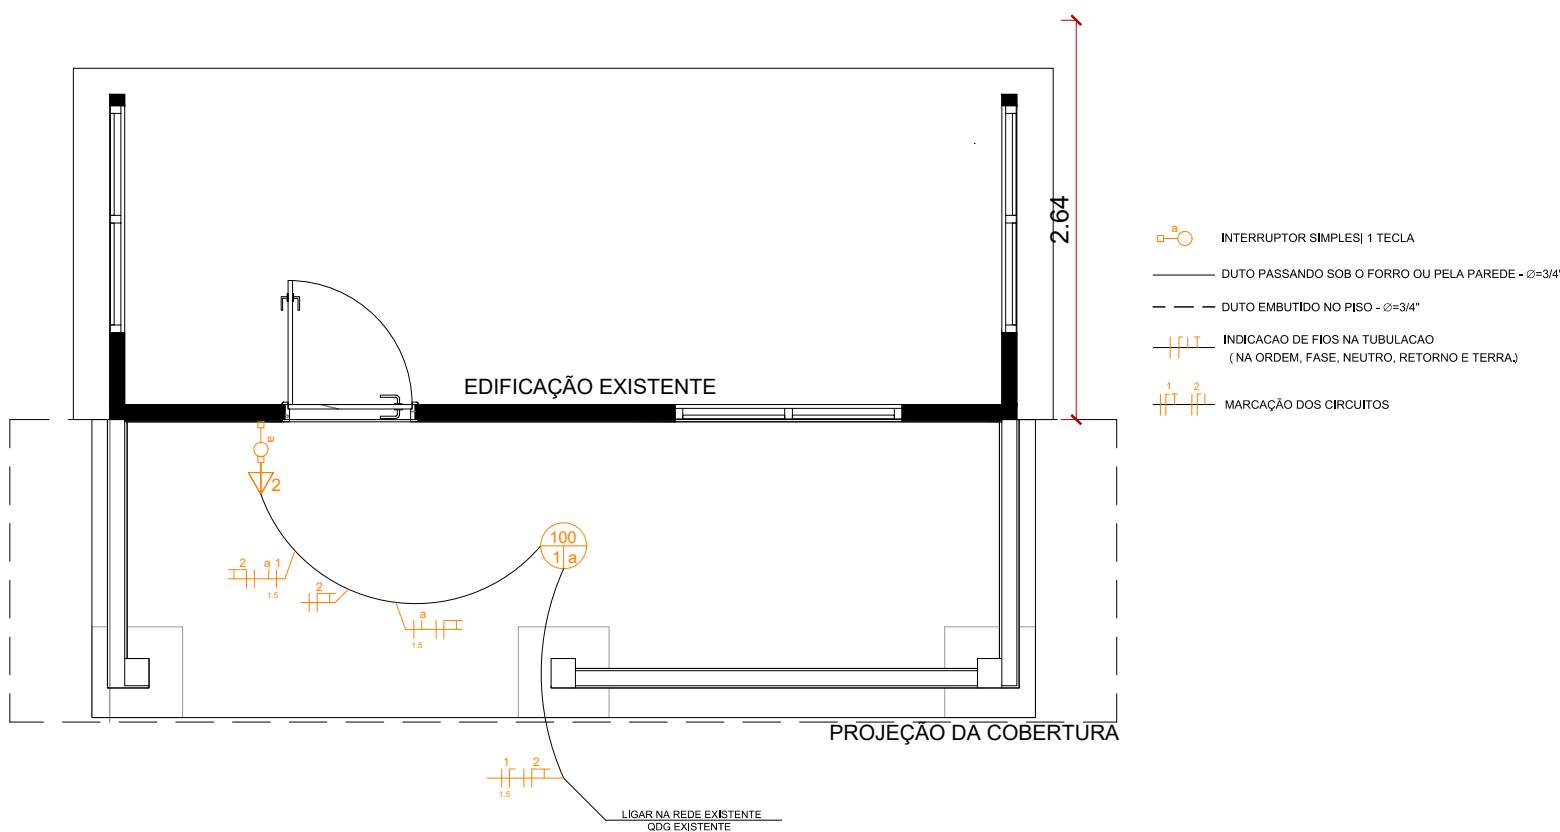

PROJETO
PLANTA ELÉTRICA
ESC: 1:50

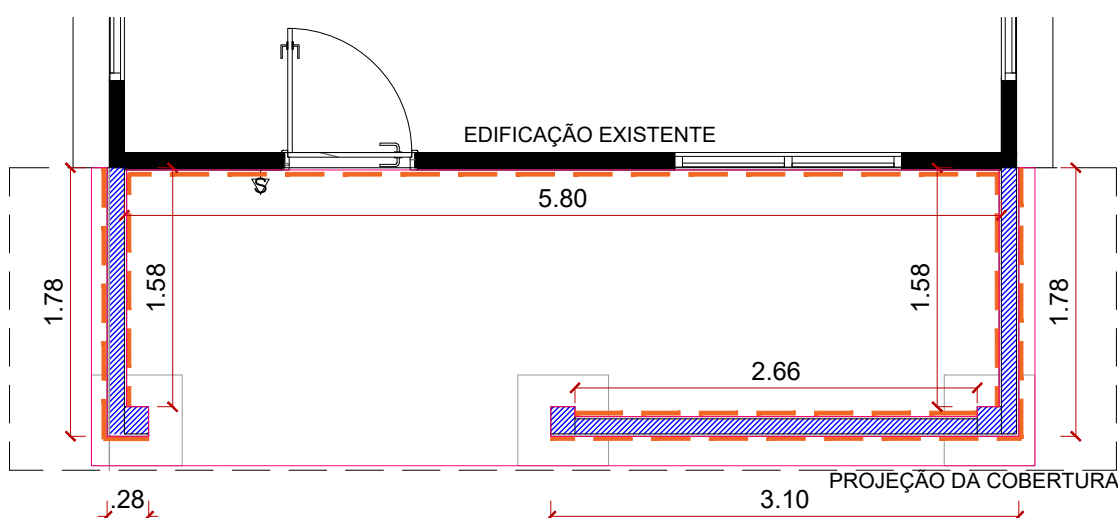

PROJETO
PLANTA BAIXA REVESTIMENTO
ESC: 1:50

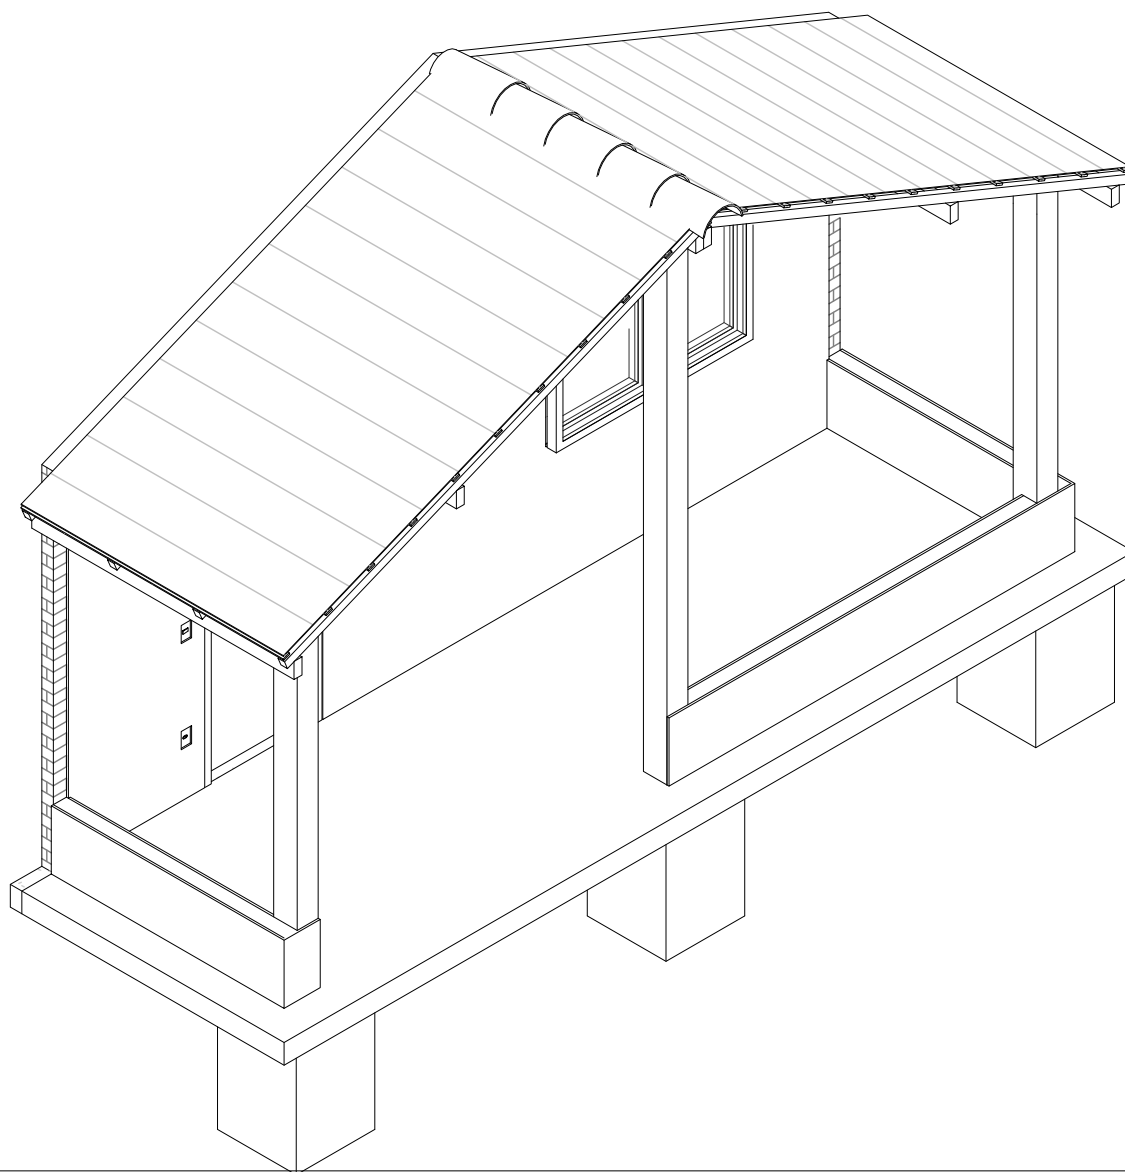

LEGENDA PAREDE			
	MASSA ÚNICA + FUNDO SELADOR + PINTURA COM TINTA TEXTURIZADA ACRÍLICA, UMA COR		
	PAREDE A CONSTRUIR		
QUADRO DE ÁREAS			
REVESTIMENTO DAS PAREDES E MURETA EXTERNAS			
MATERIAL	CÔMODO	ÁREA	
MASSA ÚNICA	VARANDA	9,35 m²	
FUNDO SELADOR	VARANDA	24,34 m²	
PINTURA TEXTURIZADA ACRÍLICA	VARANDA	24,34 m²	
QUADRO DE ÁREAS			
CÔMODO	MATERIAL	ÁREA	
VARANDA	REVESTIMENTO CERÂMICO COM PLACAS DE 35X35	9,82m²	
VARANDA	RODA PÉ CERÂMICO DE 7CM DE ALTURA	11,65 m²	
MINISTÉRIO DAS CIDADES	GRUPO: CONSTRUÇÃO, AMPLIAÇÃO E ADEQUAÇÃO DE CÔMODOS		FOLHA: 02/02
	KIT: VARANDA	CÓDIGO DO KIT: 4.7	